Republika e Kosovës
Republika Kosova-Republic of Kosova
Qeveria -Vlada-Government

Ministria e Mjedisit dhe Planifikimit Hapësinor /Ministarstvo Sredine i Prostornog Planiranja/Ministry of Environment and Spatial Planning

AGJENCIA KADASTRALE E KOSOVËS/ KATASTARSKA AGECIJA KOSOVA/ KOSOVA CADASTRAL AGENCY

Zyra kadastrale komunale / Opštinska katastarska kancelarija: Ferizaj

Nr. i njësisë kadastrale / Br. katastarske jedinice : 00041-0,00042-0,00043-0 00044-0,00045-1,00045-2

Zona kadastrale / Katastarska zona: Manastirc

Numri i lëndës / Broj predmeta: 106/2026 102/1172-140/26

Lloji i njësisë kadastrale / Vrsta katastarske jedinice : Parcel

Shkalla e zvoglimit / Razmera plana : 1:1250

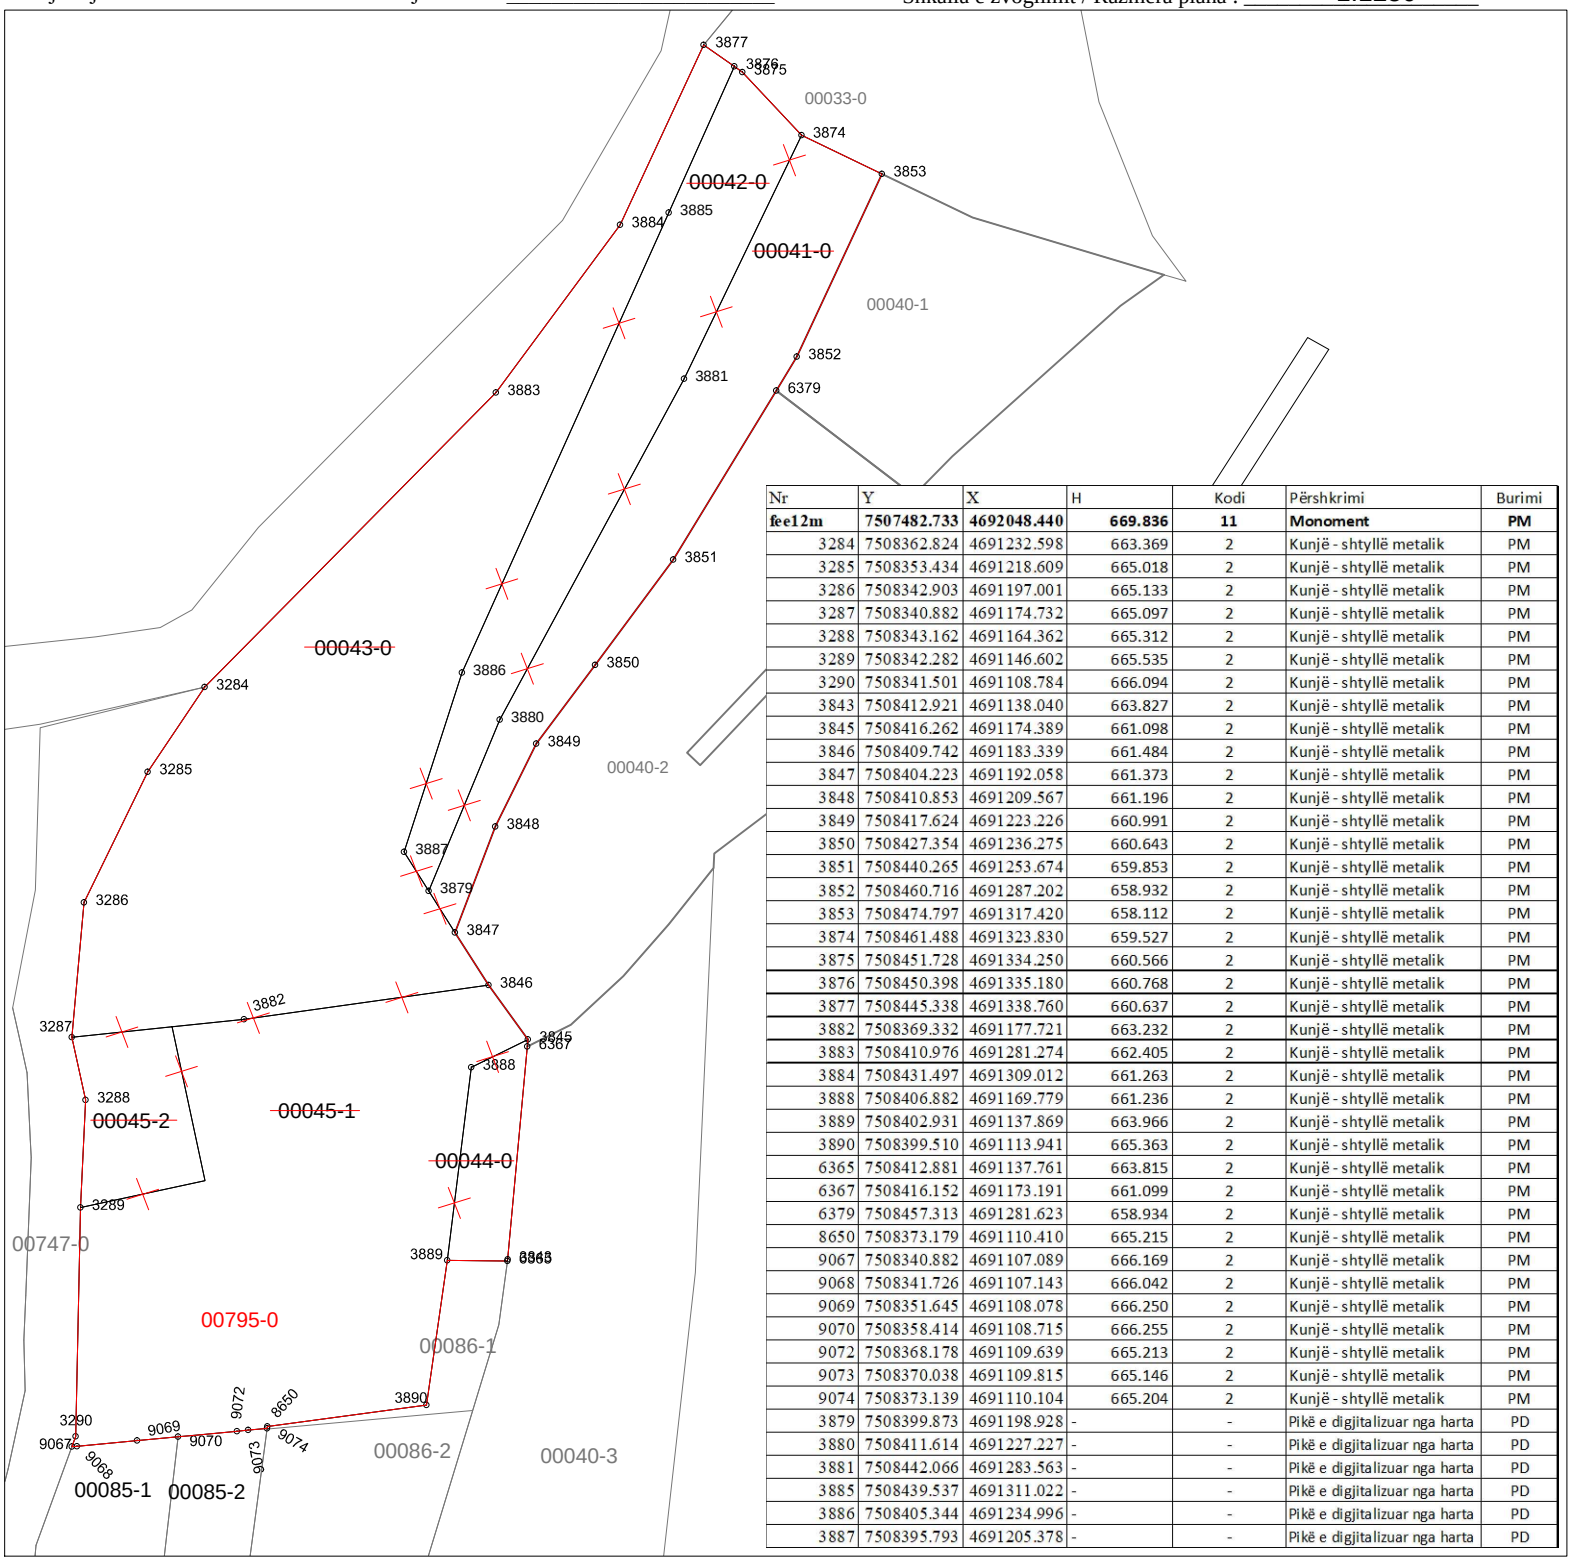

Nr	Y	X	H	Kodi	Përshkrimi	Burimi
fee12m	**7507482.733**	**4692048.440**	**669.836**	**11**	**Monoment**	**PM**
3284	7508362.824	4691232.598	663.369	2	Kunjë - shtyllë metalik	PM
3285	7508353.434	4691218.609	665.018	2	Kunjë - shtyllë metalik	PM
3286	7508342.903	4691197.001	665.133	2	Kunjë - shtyllë metalik	PM
3287	7508340.882	4691174.732	665.097	2	Kunjë - shtyllë metalik	PM
3288	7508343.162	4691164.362	665.312	2	Kunjë - shtyllë metalik	PM
3289	7508342.282	4691146.602	665.535	2	Kunjë - shtyllë metalik	PM
3290	7508341.501	4691108.784	666.094	2	Kunjë - shtyllë metalik	PM
3843	7508412.921	4691138.040	663.827	2	Kunjë - shtyllë metalik	PM
3845	7508416.262	4691174.389	661.098	2	Kunjë - shtyllë metalik	PM
3846	7508409.742	4691183.339	661.484	2	Kunjë - shtyllë metalik	PM
3847	7508404.223	4691192.058	661.373	2	Kunjë - shtyllë metalik	PM
3848	7508410.853	4691209.567	661.196	2	Kunjë - shtyllë metalik	PM
3849	7508417.624	4691223.226	660.991	2	Kunjë - shtyllë metalik	PM
3850	7508427.354	4691236.275	660.643	2	Kunjë - shtyllë metalik	PM
3851	7508440.265	4691253.674	659.853	2	Kunjë - shtyllë metalik	PM
3852	7508460.716	4691287.202	658.932	2	Kunjë - shtyllë metalik	PM
3853	7508474.797	4691317.420	658.112	2	Kunjë - shtyllë metalik	PM
3874	7508461.488	4691323.830	659.527	2	Kunjë - shtyllë metalik	PM
3875	7508451.728	4691334.250	660.566	2	Kunjë - shtyllë metalik	PM
3876	7508450.398	4691335.180	660.768	2	Kunjë - shtyllë metalik	PM
3877	7508445.338	4691338.760	660.637	2	Kunjë - shtyllë metalik	PM
3882	7508369.332	4691177.721	663.232	2	Kunjë - shtyllë metalik	PM
3883	7508410.976	4691281.274	662.405	2	Kunjë - shtyllë metalik	PM
3884	7508431.497	4691309.012	661.263	2	Kunjë - shtyllë metalik	PM
3888	7508406.882	4691169.779	661.236	2	Kunjë - shtyllë metalik	PM
3889	7508402.931	4691137.869	663.966	2	Kunjë - shtyllë metalik	PM
3890	7508399.510	4691113.941	665.363	2	Kunjë - shtyllë metalik	PM
6365	7508412.881	4691137.761	663.815	2	Kunjë - shtyllë metalik	PM
6367	7508416.152	4691173.191	661.099	2	Kunjë - shtyllë metalik	PM
6379	7508457.313	4691281.623	658.934	2	Kunjë - shtyllë metalik	PM
8650	7508373.179	4691110.410	665.215	2	Kunjë - shtyllë metalik	PM
9067	7508340.882	4691107.089	666.169	2	Kunjë - shtyllë metalik	PM
9068	7508341.726	4691107.143	666.042	2	Kunjë - shtyllë metalik	PM
9069	7508351.645	4691108.078	666.250	2	Kunjë - shtyllë metalik	PM
9070	7508358.414	4691108.715	666.255	2	Kunjë - shtyllë metalik	PM
9072	7508368.178	4691109.639	665.213	2	Kunjë - shtyllë metalik	PM
9073	7508370.038	4691109.815	665.146	2	Kunjë - shtyllë metalik	PM
9074	7508373.139	4691110.104	665.204	2	Kunjë - shtyllë metalik	PM
3879	7508399.873	4691198.928	-	-	Pikë e digjitalizuar nga harta	PD
3880	7508411.614	4691227.227	-	-	Pikë e digjitalizuar nga harta	PD
3881	7508442.066	4691283.563	-	-	Pikë e digjitalizuar nga harta	PD
3885	7508439.537	4691311.022	-	-	Pikë e digjitalizuar nga harta	PD
3886	7508405.344	4691234.996	-	-	Pikë e digjitalizuar nga harta	PD
3887	7508395.793	4691205.378	-	-	Pikë e digjitalizuar nga harta	PD

Rilevoi / Snimio: LIRIDON SEJDIU
(emri dhe mbiemri i gjeodetit/kompanisë/ ime i prezime geodeta/ kompanije)

Aprovoi / Usvojio: _____
(emri dhe mbiemri i përsonit zyrtar/ ime i prezime sluzbenog lica)

Nr. i licencës / Br. licence: 140

V.V.

Nënshkrimi / Potpis: _____

Nënshkrimi / Potpis: _____

Data e rilevimit / Datum snimanja: 04.05.2026

Data e aprovimit / Datum usvajanja: _____