Republika e Kosovës
Republika Kosova-Republic of Kosova
Qeveria -Vlada-Government
Ministria e Mjedisit dhe Planifikimit Hapësinor /Ministarstvo Sredine i Prostornog Planiranja/Ministry of Environment and Spatial Planning
AGJENCIA KADASTRALE E KOSOVËS/ KATASTARSKA AGECIJA KOSOVA/ KOSOVA CADASTRAL AGENCY

Zyra kadastrale komunale / Opštinska katastarska kancelarija: Ferizaj

Nr. i njësisë kadastrale / Br. katastarske jedinice : 00045-1,00045-2

Zona kadastrale / Katastarska zona: Manastirc

Numri i lëndës / Broj predmeta: 091/2026 83/1172-140/26

Lloji i njësisë kadastrale / Vrsta katastarske jedinice : Parcel

Shkalla e zvoglimit / Razmera plana : 1:500

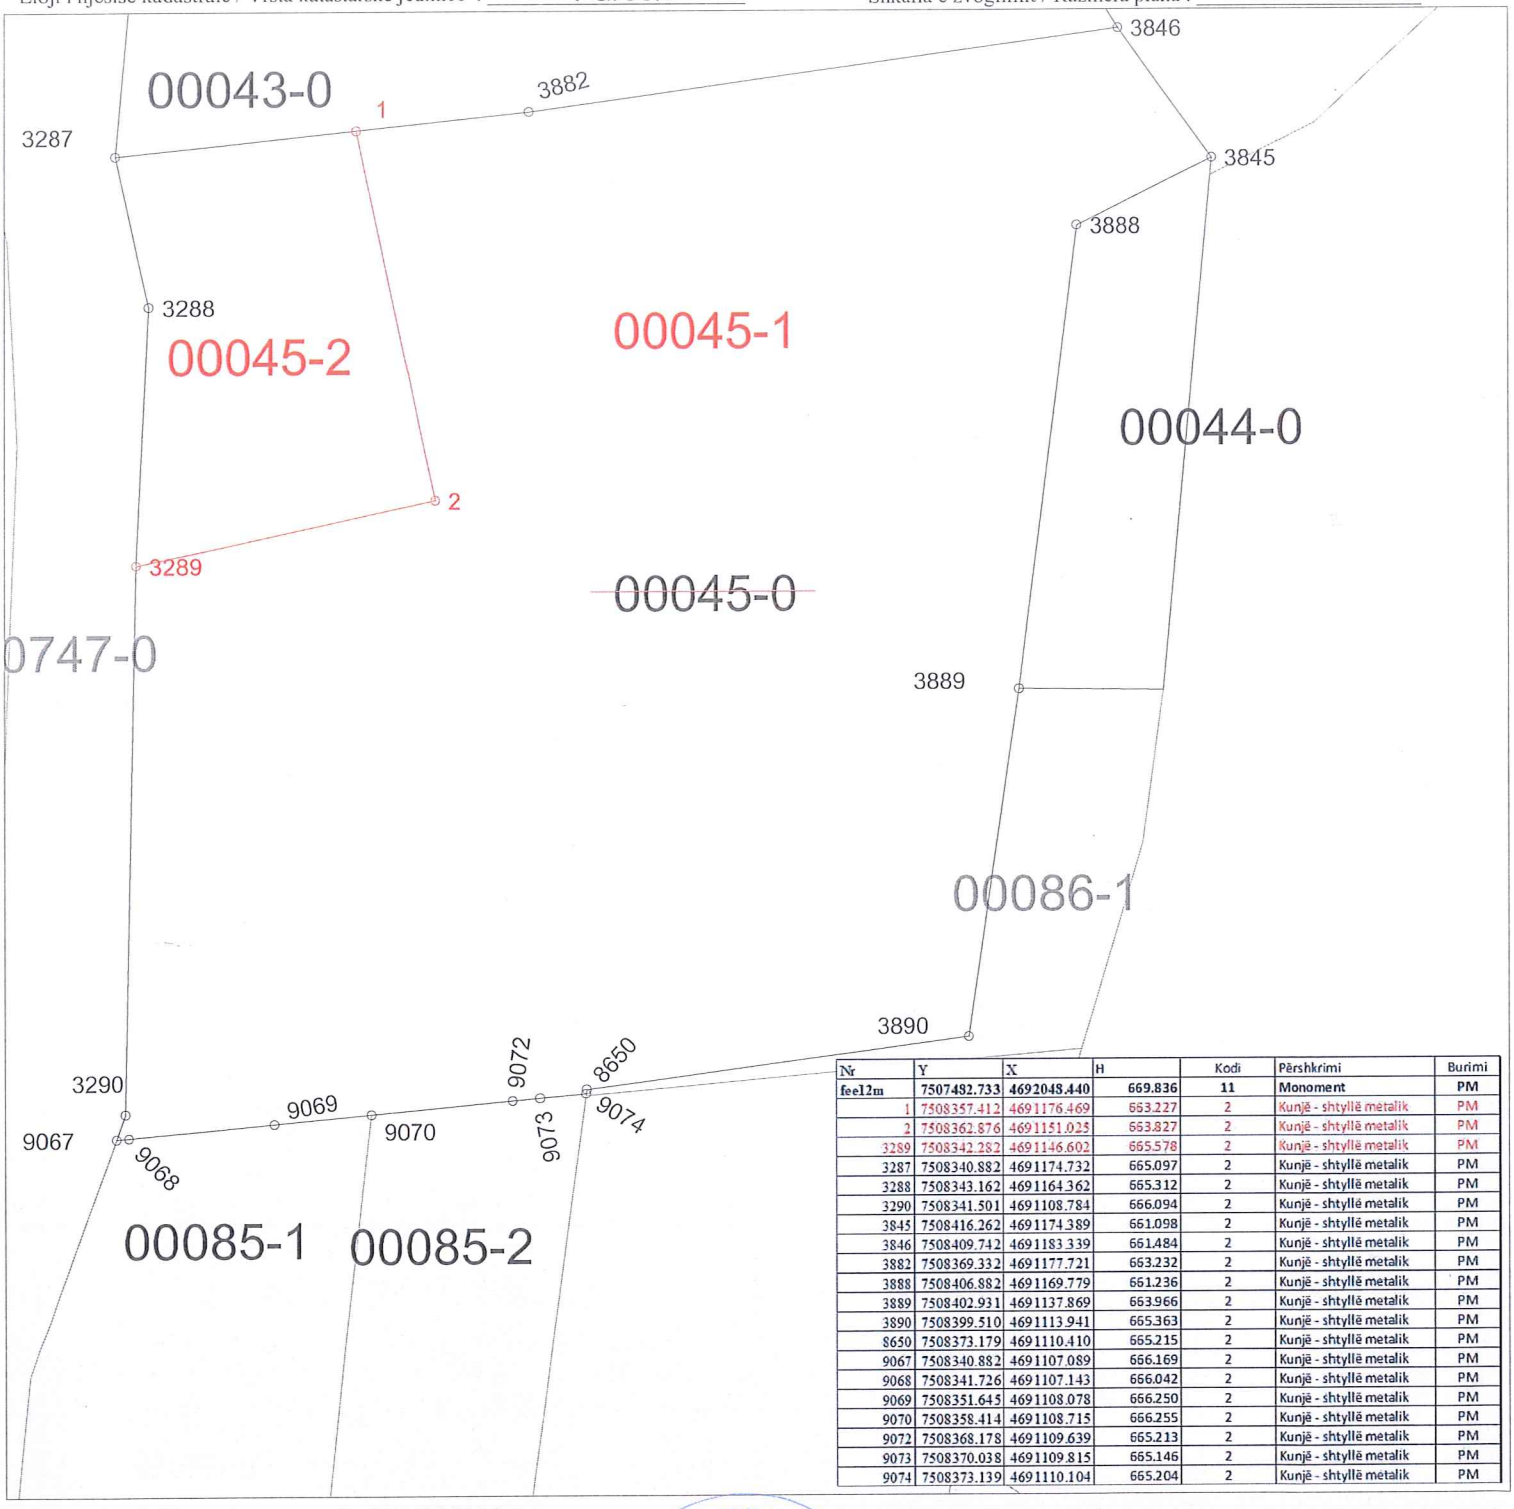

Nr	Y	X	H	Kodi	Përshkrimi	Burimi
fee12m	7507482.733	4692048.440	669.836	11	Monoment	PM
1	7508357.412	4691176.469	663.227	2	Kunjë - shtyllë metalik	PM
2	7508362.876	4691151.025	663.827	2	Kunjë - shtyllë metalik	PM
3289	7508342.282	4691146.602	665.578	2	Kunjë - shtyllë metalik	PM
3287	7508340.882	4691174.732	665.097	2	Kunjë - shtyllë metalik	PM
3288	7508343.162	4691164.362	665.312	2	Kunjë - shtyllë metalik	PM
3290	7508341.501	4691108.784	666.094	2	Kunjë - shtyllë metalik	PM
3845	7508416.262	4691174.389	661.098	2	Kunjë - shtyllë metalik	PM
3846	7508409.742	4691183.339	661.484	2	Kunjë - shtyllë metalik	PM
3882	7508369.332	4691177.721	663.232	2	Kunjë - shtyllë metalik	PM
3888	7508406.882	4691169.779	661.236	2	Kunjë - shtyllë metalik	PM
3889	7508402.931	4691137.869	663.966	2	Kunjë - shtyllë metalik	PM
3890	7508399.510	4691113.941	665.363	2	Kunjë - shtyllë metalik	PM
8650	7508373.179	4691110.410	665.215	2	Kunjë - shtyllë metalik	PM
9067	7508340.882	4691107.089	666.169	2	Kunjë - shtyllë metalik	PM
9068	7508341.726	4691107.143	666.042	2	Kunjë - shtyllë metalik	PM
9069	7508351.645	4691108.078	666.250	2	Kunjë - shtyllë metalik	PM
9070	7508358.414	4691108.715	666.255	2	Kunjë - shtyllë metalik	PM
9072	7508368.178	4691109.639	665.213	2	Kunjë - shtyllë metalik	PM
9073	7508370.038	4691109.815	665.146	2	Kunjë - shtyllë metalik	PM
9074	7508373.139	4691110.104	665.204	2	Kunjë - shtyllë metalik	PM

Rilevoi / Snimio: LIRIDON SEJDIU
(emri dhe mbiemri i gjeodetit/kompanisë/ ime i prezime geodeta/ kompanije)

Nr. i licencës / Br. licence: 140

Nënshkrimi / Potpis:

Data e rilevimit / Datum snimanja: 22.04.2026

GJEODETI I LICENCUAR - LICENCIRANI GEODETA - FERIZAJ-UROŠEVAC - LIRIDON A. SEJDIU

V.V.

Aprovoi / Usvojio:
(emri dhe mbiemri i përsonit zyrtar/ ime i prezime sluzbenog lica)

Nënshkrimi / Potpis:

Data e aprovimit / Datum usvajanja: